


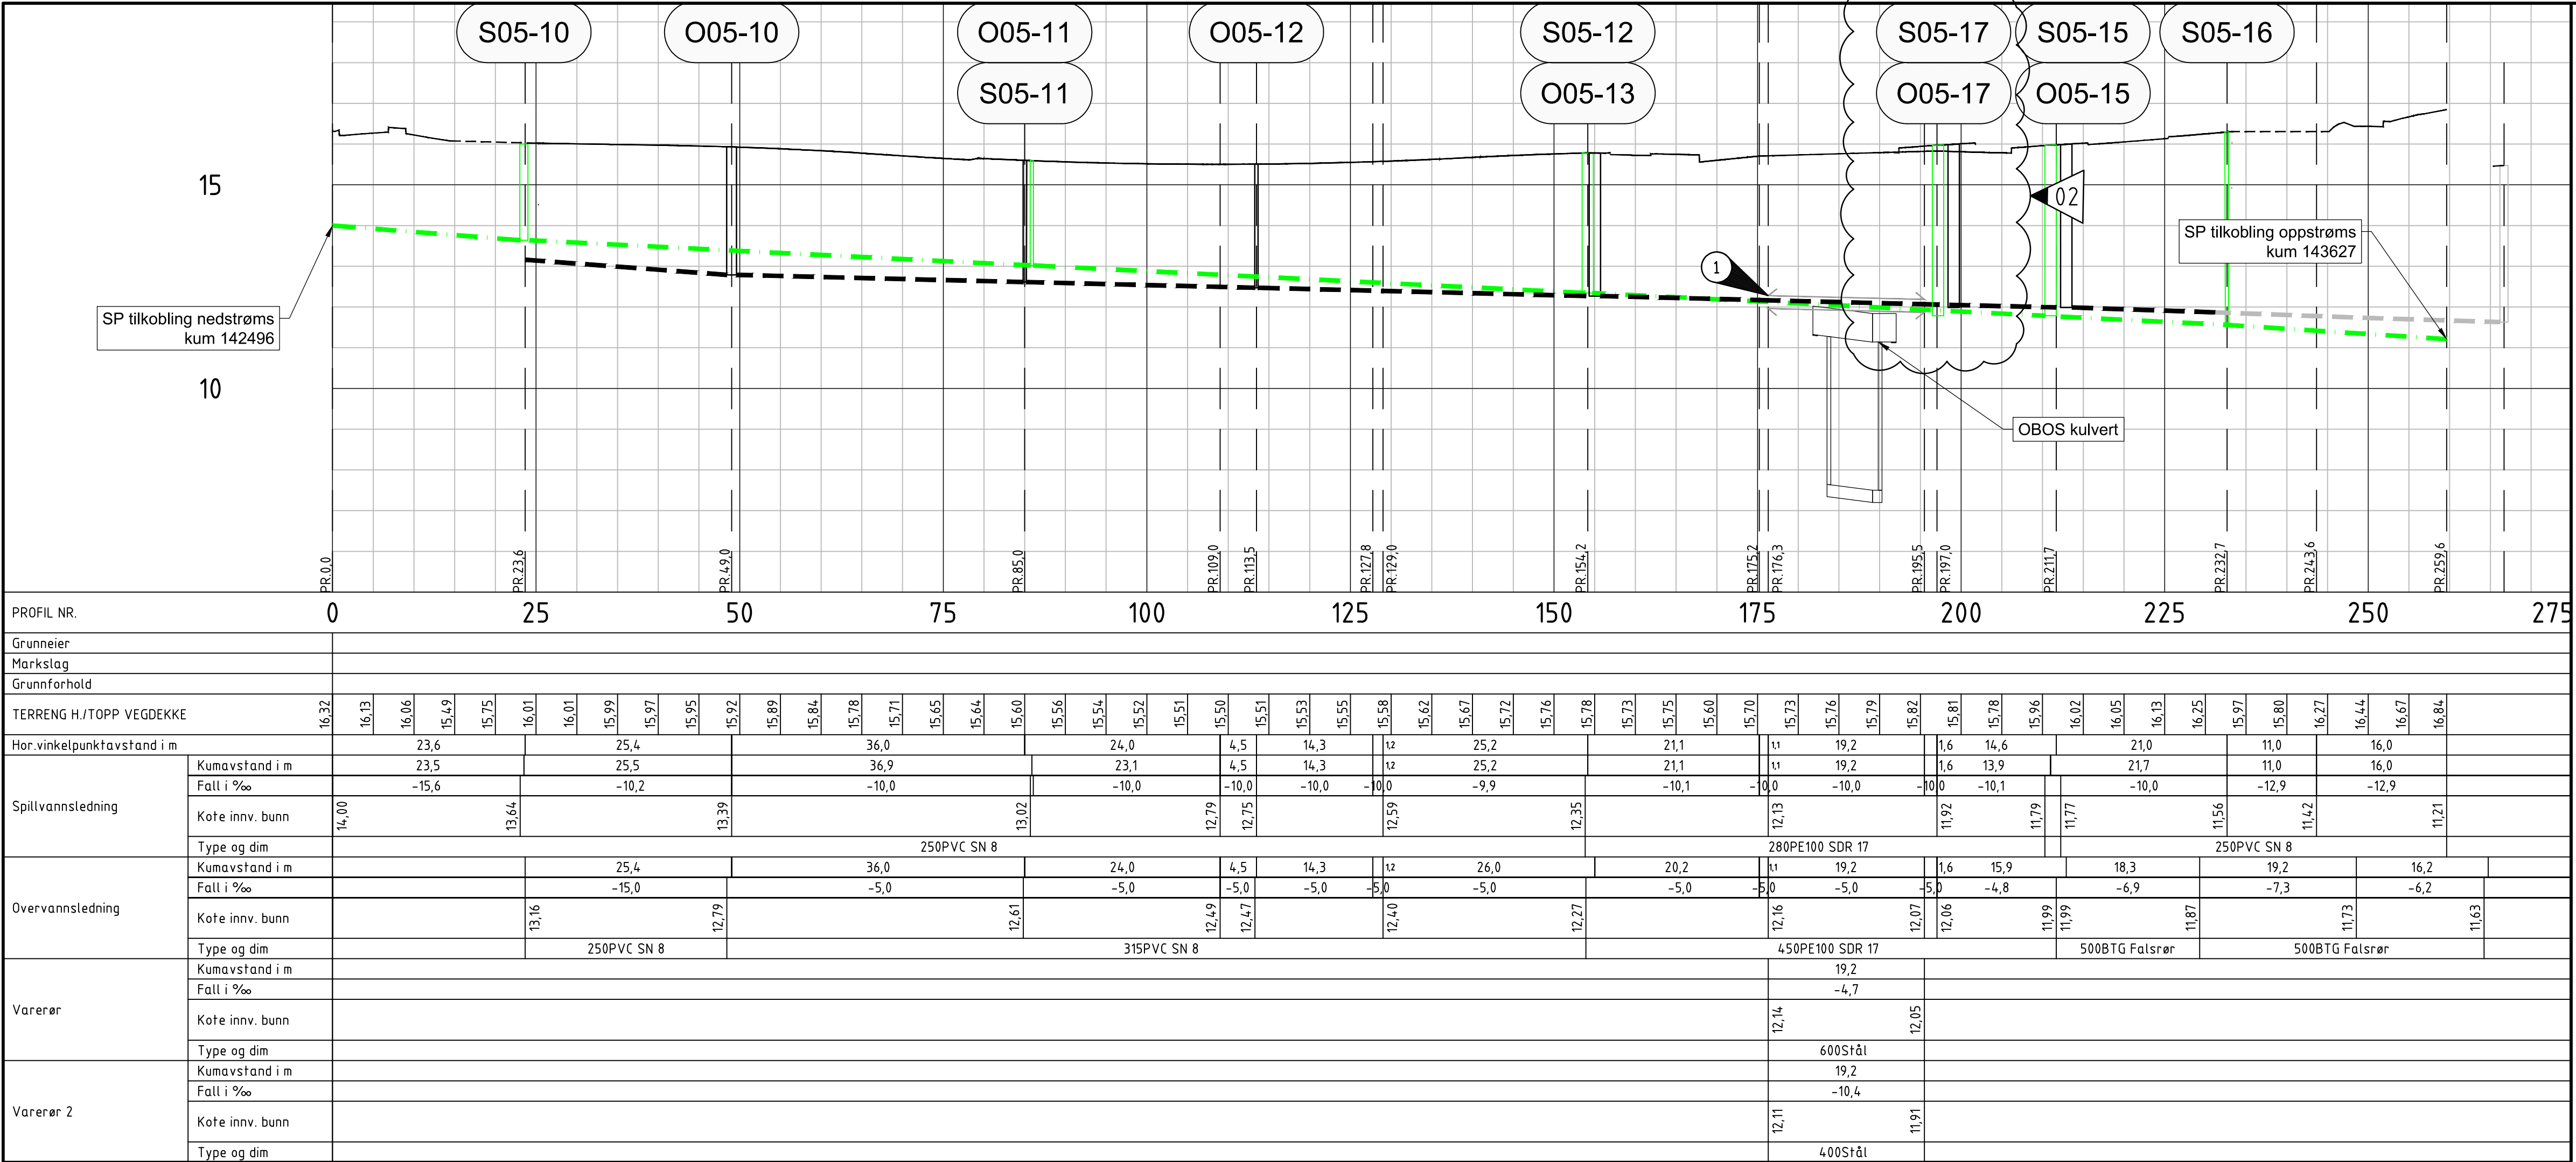

Tegnforklaring

Overvannsledning

Pumpe overvannsledning

Vannledning

Spillvannsledning

Pumpe spillvannsledning

Drensledning

Eksisterende

Prosjektert

Kommunal/privat

Utgår

Vannkum

Brannkum

Spillvannskum

Overvannskum

Sandfang

Hjelpesluk

Fordrøyningsmagasin

Varerør

Linjedren

Eiendomsgrenser

Spunt (entreprise K2A)

Eksist. teknisk kulvert

Se RIB modell for kulvert forlengelse

oooooooooooooooo


Henvisninger

PF-FLY0-731-XH-0003; FLY Overordnet VA-plan
PF-FLY0-731-XH-0005; FLY Overordnet VA-plan - Permanent; Flytårnet stasjon og Snarøyveien

Merknader

Materiell og utførelse skal være i henhold til Bærum kommunes VA-norm.
Fornebubanen sine arbeider med nye Flytårnet stasjon er delt inn i to entrepriser og VA-arbeidene vil bygges på ulike tidspunkter i entreprise K6 (Flytårnet) og Snarøyveien. Tegningen illustrerer hvordan permanent VA-plan kan se ut ved ferdigstillelse av Flytårnet stasjon og Snarøyveien.
Kumnavn og ledningsdimensjon er for Flytårnet stasjon og veidrenering i Snarøyveien er ikke oppgitt.
Drensledninger i Snarøyveien vises ikke.

1 Varerør over OBOS kulvert bygges i en annen entreprise.

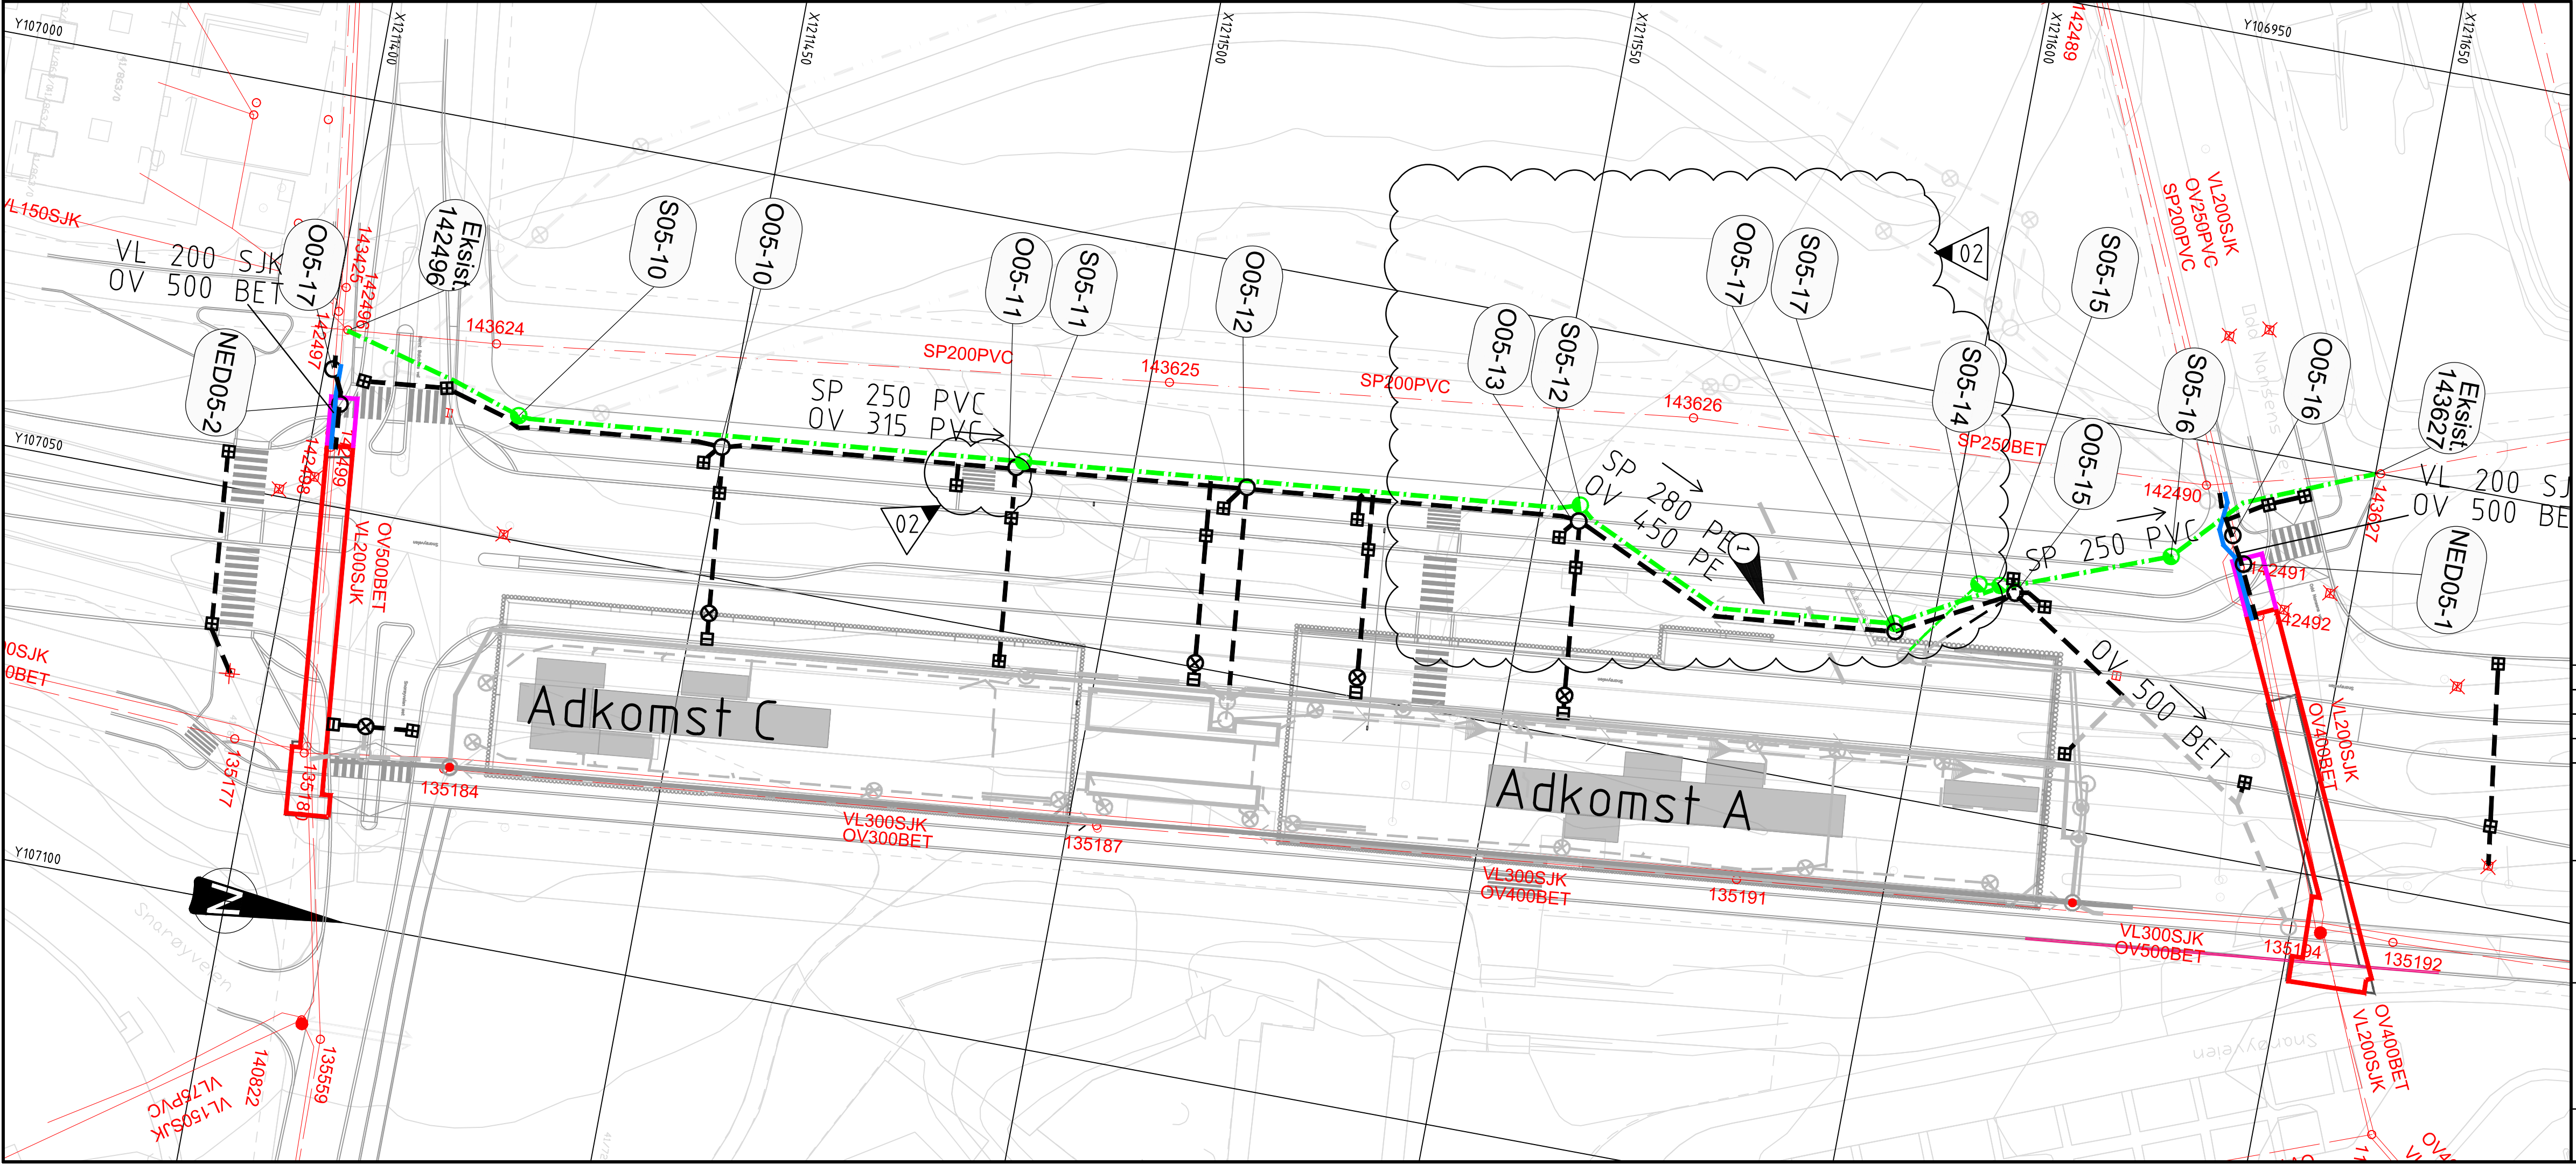

02

OFFENTLIG

02 G	Til gjennomsyn	03.05.24	PGF	SEAS	AMIK	ANS
01 G	Til gjennomgang	15.12.23	PGF	SEAS	AMIK	ANS
Rev/Status	Endring/erstatning	Dato	Leverandør	Utarb.av	Konfr.	Godkj.
Oslo		Erstattet av		Kodemanual		
Erstatning for		Erstattet for		K2-IE-OS0000-110-AC-0001		
Oppdragsgiver		Bane/Linje/Område		Prosj. nr.		
Fornebubanen		Fornebubanen		A103106 / 10201070		
Trasé/Sted/Stasjon/Entreprise		Flytårnet stasjon		Målestokk		
Tittel		FLY Overordnet VA-plan og profil og veidrenering i Snarøyveien		A1: 1:500		
Tegn. nr.		PF-FLY0-731-XH-0224		A3: 1:1000		
Blad		1		Anfall		1
Status		G		PGF		
Rådgiver		PGF		Rådgiver		